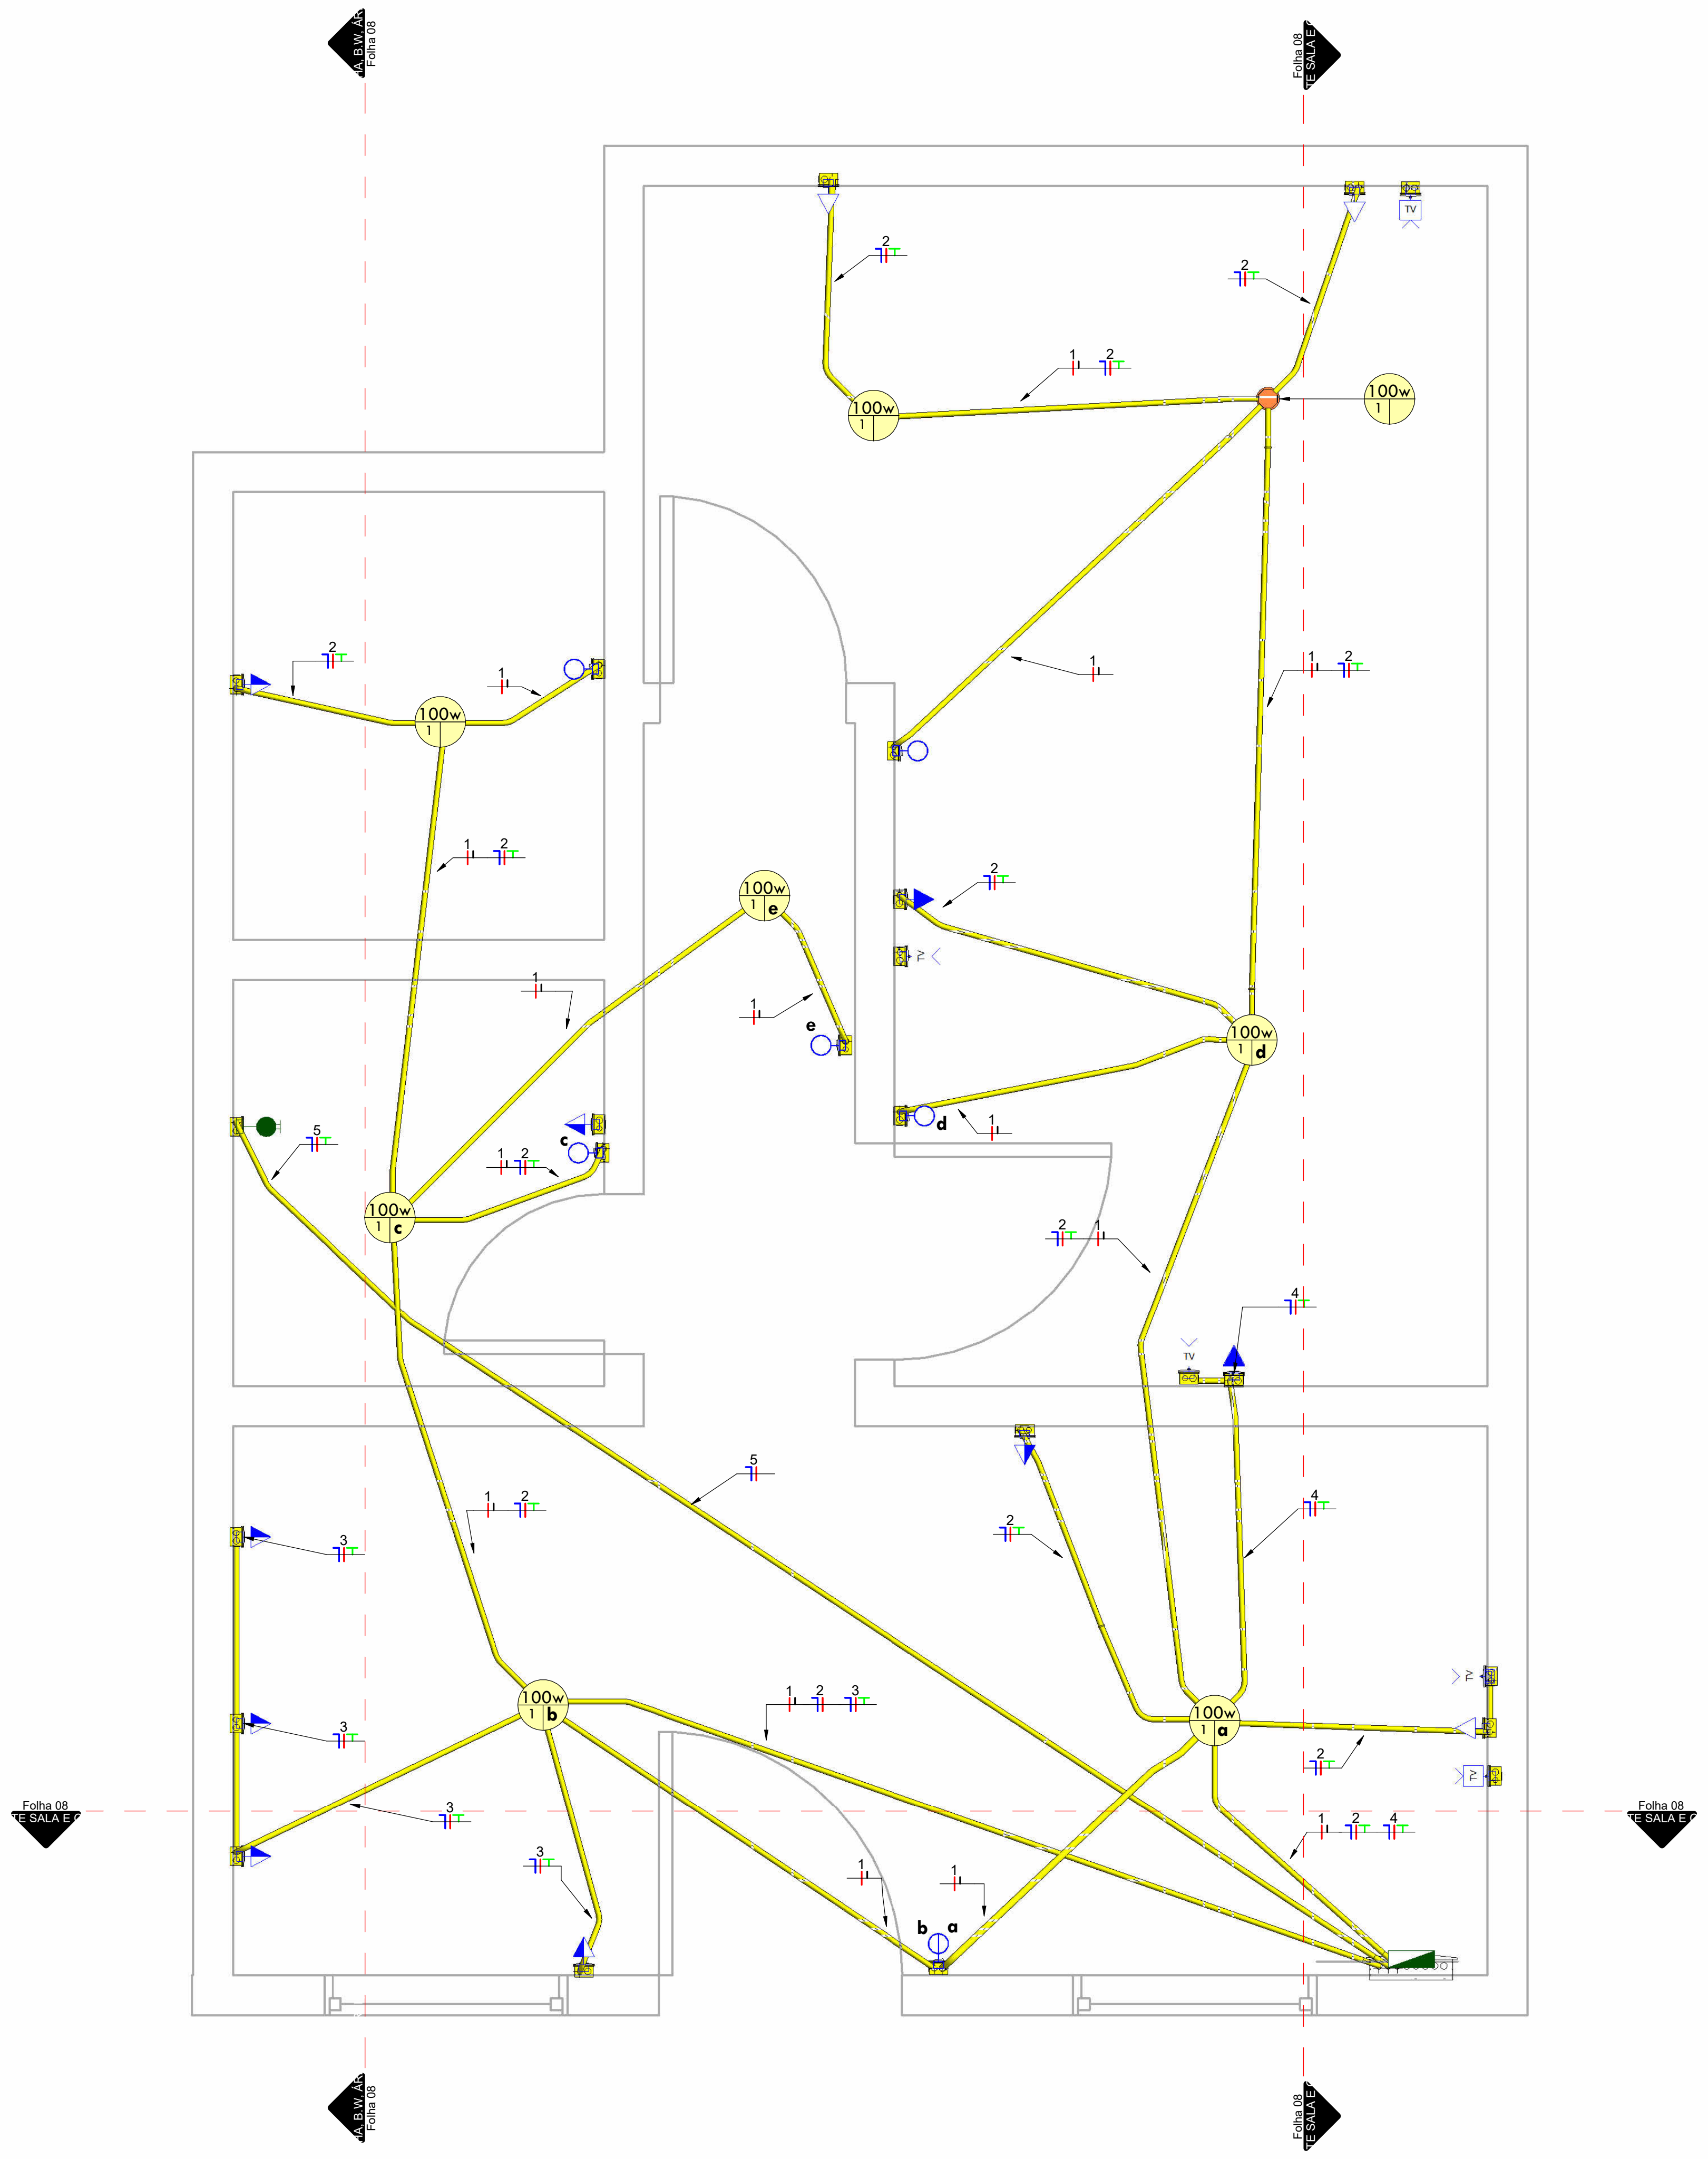

01 - PLANTA BAIXA ESTALAÇÕES ELÉTRICAS

DIAGRAMA UNIFILA

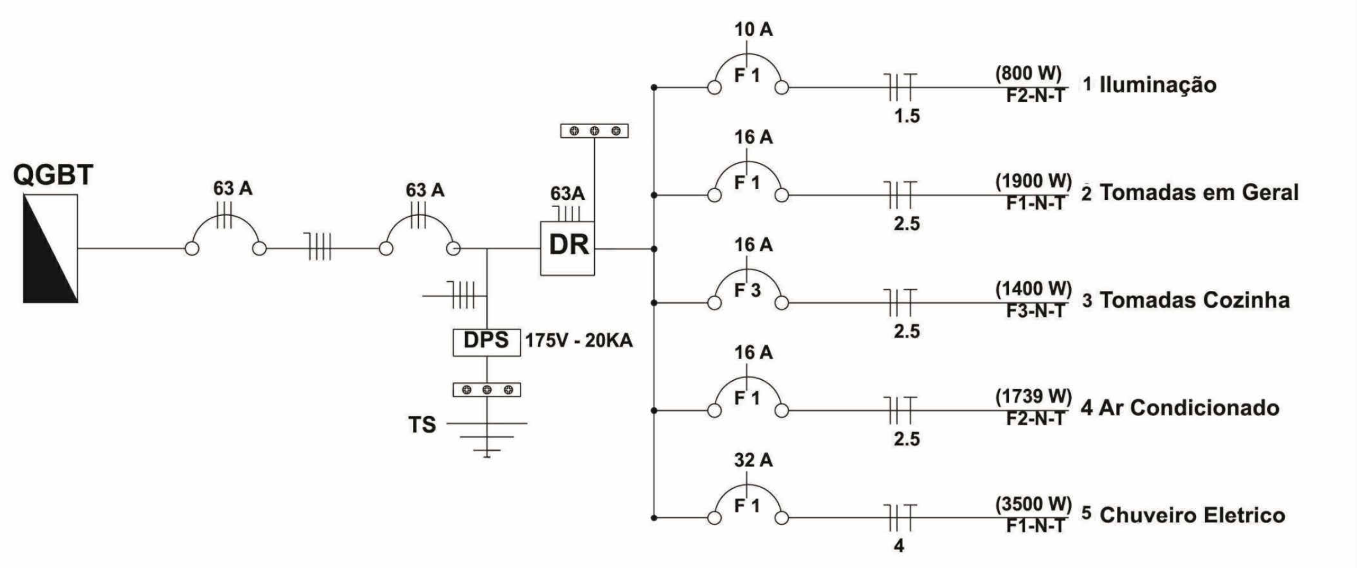

LEGENDA DIAGRAMAS UNIFILARES	
⌒	Disjuntor Termomagnético Monopolar
⌒	Disjuntor Termomagnético Bipolar
⌒	Disjuntor Termomagnético Tripolar
╫	Condutores Neutro, Fase, Terra, respectivamente
DPS	DPS-Dispositivo de proteção contra surtos
DR	IDR-Interruptor Diferencial Residual (Imax=30mA)

LEGENDA DIAGRAMA UNIFILAR

RESIDENCIAL
MATILDE VILLE – Casa 34m²

Ramal de Entrada
Concessionária: Enel/Eletropaulo 127V/220V
Nível de Tensão: 127V/220V

Fases	C. fase (mm²)	C. neutro (mm²)	D. do medidor (A)	C. terra (mm²)	Disjuntor Geral (A	P.Instalada (kW)	P. Demandada (kW)
1	16	16	63	16	63	7,56	6,63

Quadro de Cargas

Circuito	Seção (mm²)	Disjuntor In(A)	Tensão (V)	Potência (VA)	Corrente (A)	Agrupamento	C. de Condução (A	Descrição
1	1,5	10	127	800	1,26	3	12,25	Iluminação
2	2,5	16	127	1900	11,02	3	16,8	Tomadas TUGs
3	2,5	16	127	1400	11,02	3	16,8	Tomadas Coz..
4	2,5	16	127	1739	13,69	3	16,8	Ar condicionado 12kBTU
5	4	32	127	3500	27,56	1	32	Chuveiro

Eletrodutos

Item	Discriminação	Ocupação (mm²)	Ocup. maxima 40% (mm²)	N: Condutores	N: Circuitos
1	Conduite PVC Flex 3/4"	82	86	9	3

Corrente Demandada (A) por fase			
	A	B	C
Total	56,63	--	--

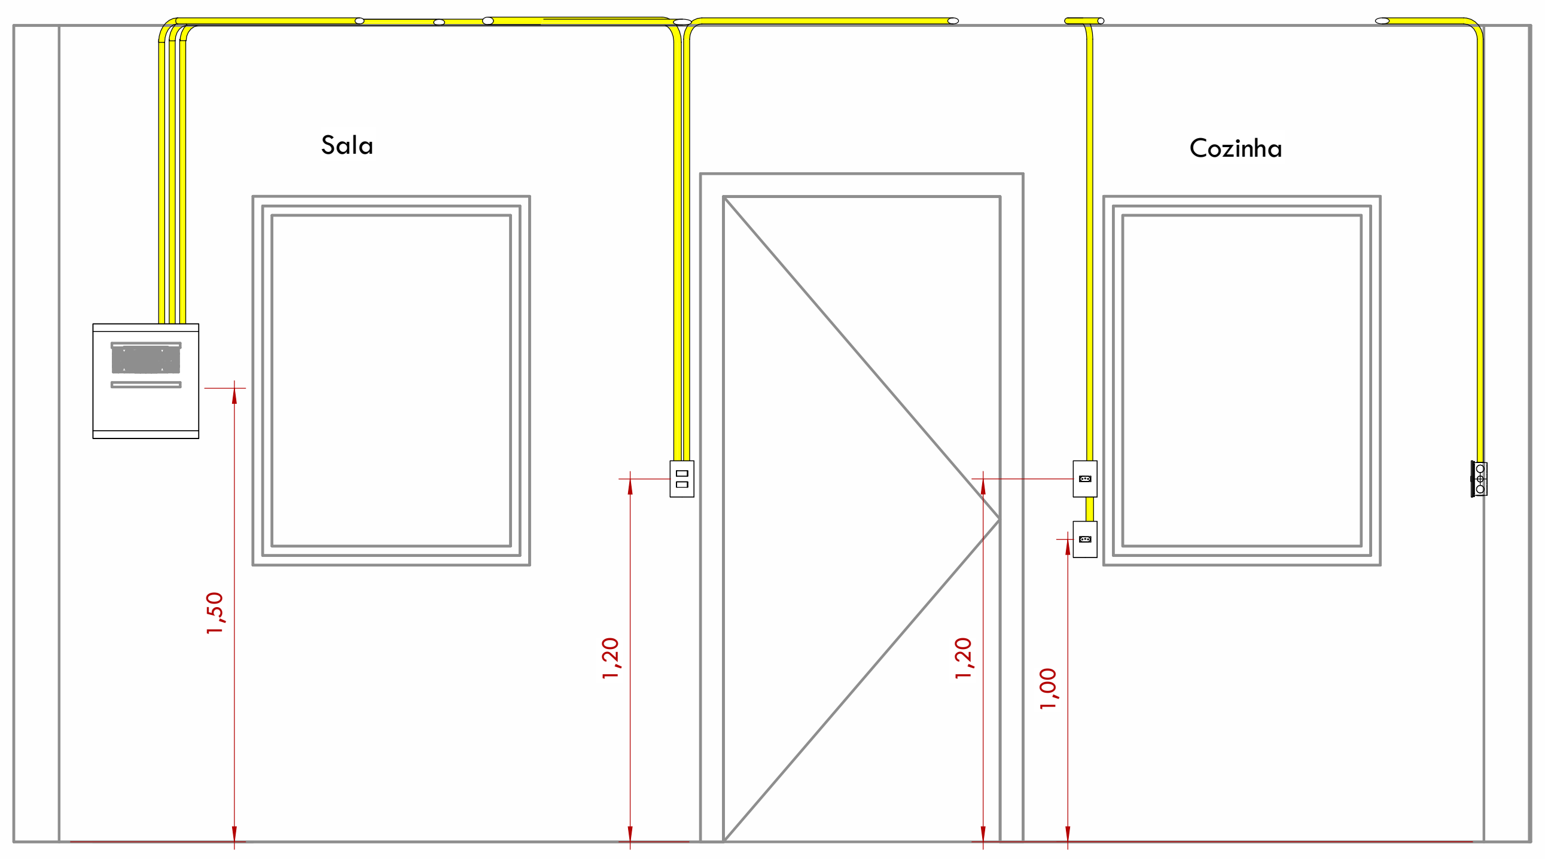

02 - CORTE SALA E COZINHA

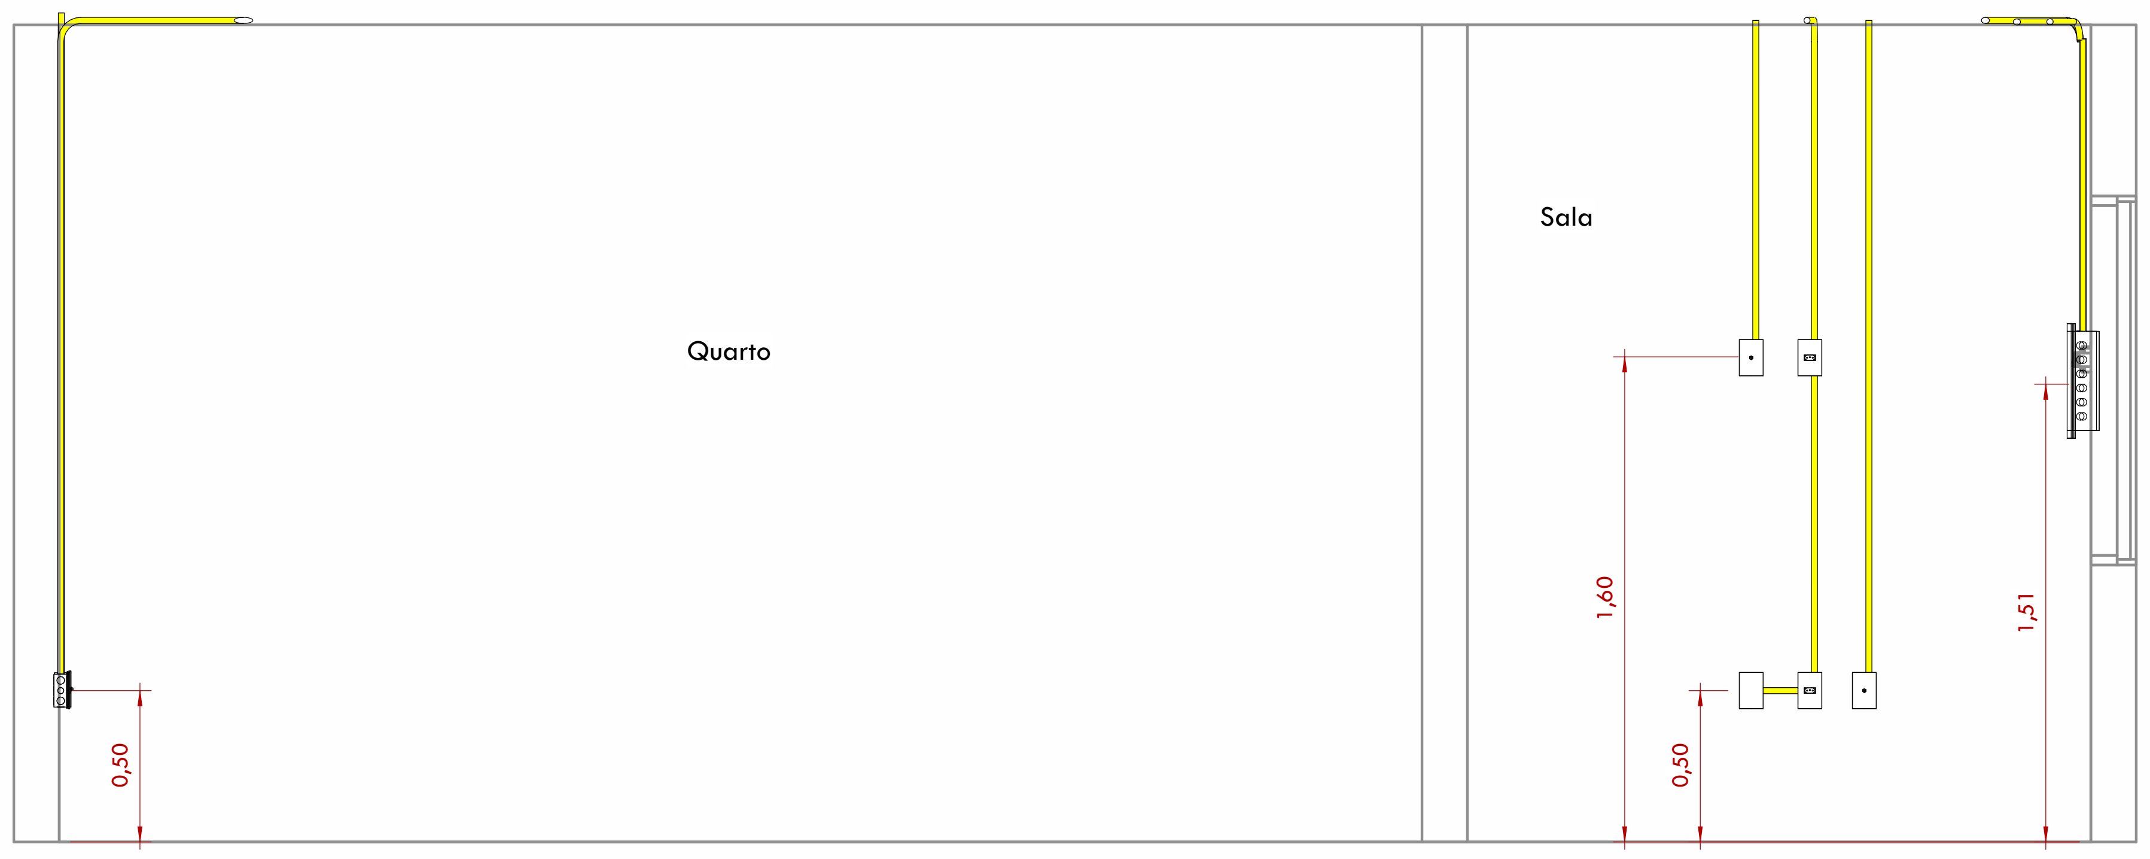

03 - CORTE SALA E QUARTO

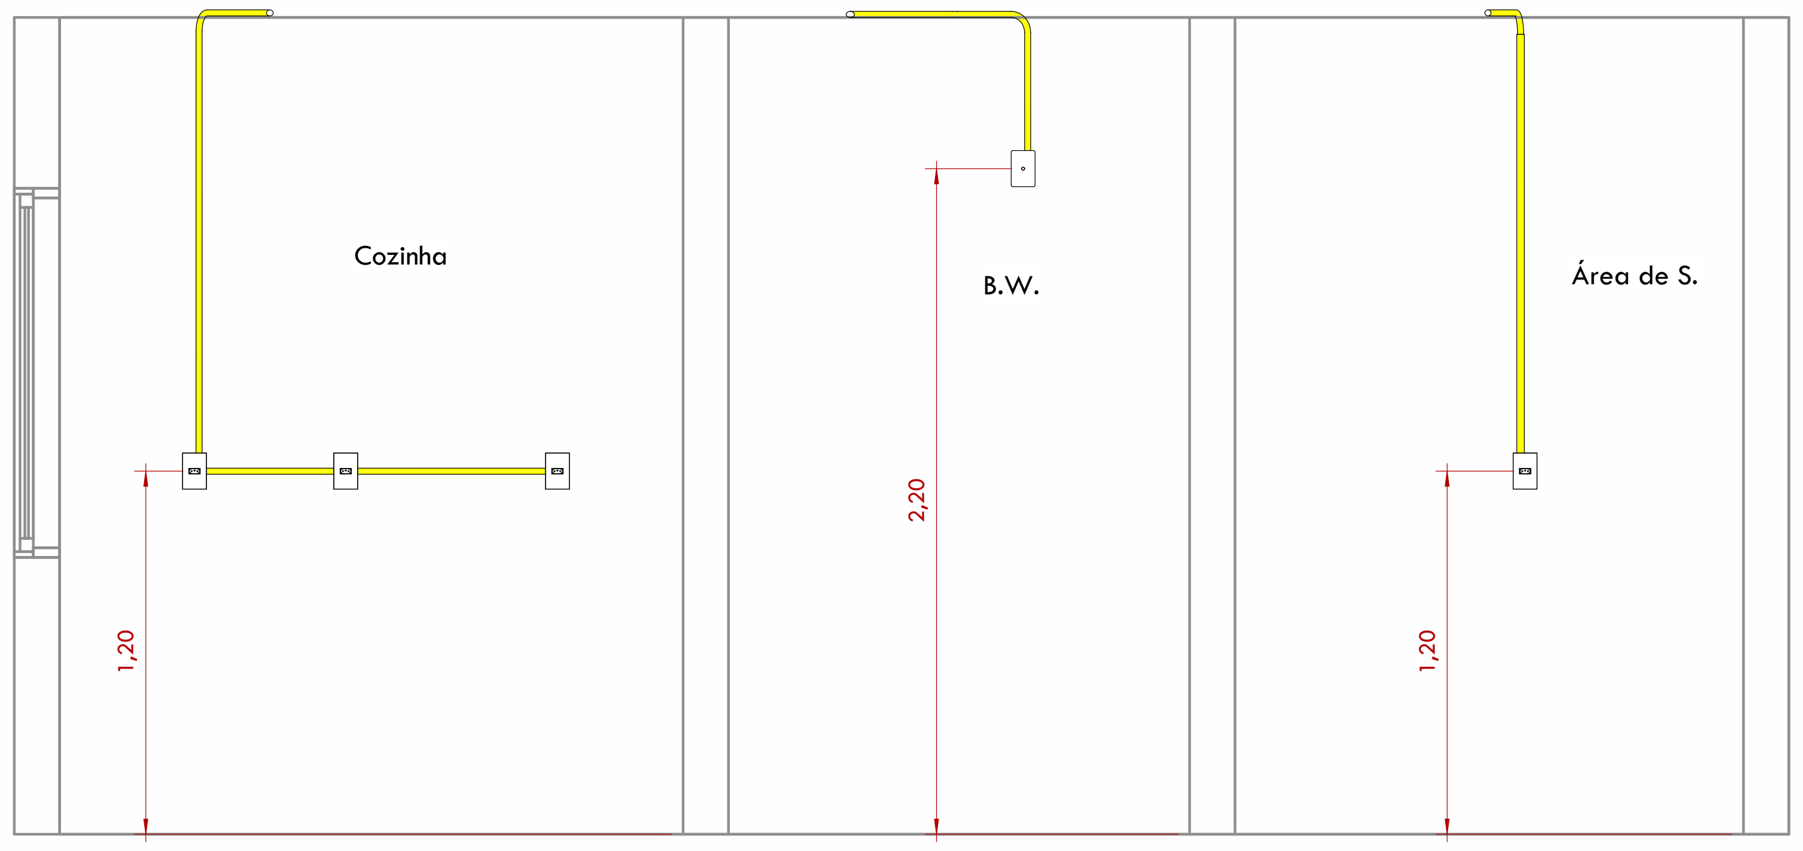

04 - CORTE COZINHA, B.W. ÁREA DE SERVIÇOS

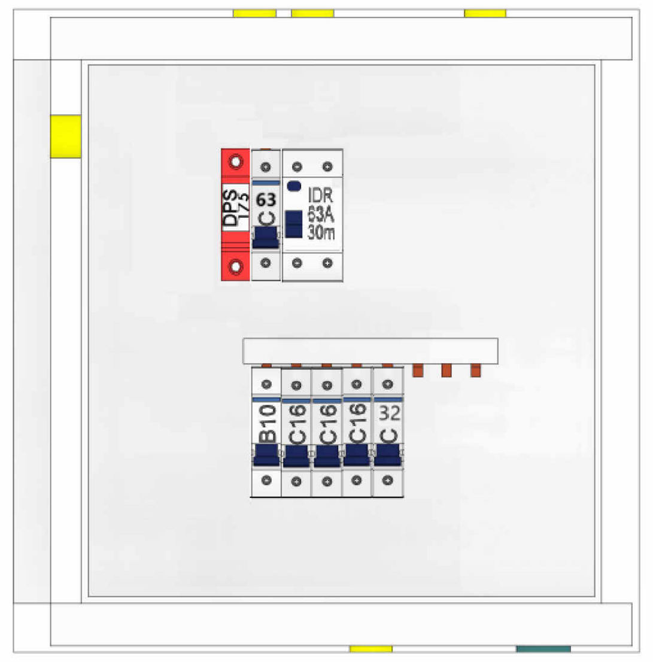

3 VISTA 3D QDC

SIMBOLOGIA ELÉTRICA	
▷	Tomada Baixa 2P+T, 10A, a 0,30 m do piso, embutido em caixa 4x2
▶	Tomada Média 2P+T, 10A, a 1,10 m do piso, embutido em caixa 4x2
▶	Tomada Alta 2P+T, 10A, a 2,10 cm do piso, embutido em caixa 4x2
▷	Tomada Baixa 2P+T, 20A, a 0,30 m do piso, embutido em caixa 4x2
▶	Tomada Média 2P+T, 20A, a 1,10 m do piso , embutido em caixa 4x2
▶	Tomada Alta 2P+T, 20A, a 2,10 m do piso , embutido em caixa 4x2
▷	Tomada de Piso 2P+T, 10A
▶	Tomada de Teto 2P+T, 20A
⭠	Módulo de tomada USB
⊖	Ponto de Força com placa saída de fio, a 220cm do piso acabado
⊖	Ponto de Força com placa saída de fio, a "x" cm do piso acabado
○ a	Interruptor simples de uma seção, embutido em caixa 4x2
● a	Interruptor paralelo, embutido em caixa 4x2
◒ a	Interruptor intermediário, embutido em caixa 4x2
⊙ a	Pulsador
☐	Ponto para campainha
⊙ a	Dimer (Variador de Luminosidade)
◗ a	Sensor de presença, embutido em caixa 4x2
100w 10 a	Ponto de luz embutido no teto
100w 1 a	Ponto de luz na parede para arandela
●	Ponto de luz na parede para fita LED
——	Eletroduto embutido no teto ou na parede
- - - -	Eletroduto embutido no piso
◢	Quadro geral de luz e força embutido a 1,50 do piso acabado
MED	Caixa para medidor
⊠	Caixa de passagem no piso
CPT ⊠	Caixa de passagem de passagem CPT de embutir na parede
⊠	Caixa de passagem de passagem 4X2" ou 4x4" de embutir na parede
↗	Eletroduto que sobe
↙	Eletroduto que desce
↙	Eletroduto que passa descendo
↗	Eletroduto que passa subindo
╫	Condutores Neutro, Fase, Terra e Retorno, respectivamente
A ▲	Simbologia de elevação

Observações:

SIMBOLOGIA ELÉTRICA

LEGENDA ELETRODUTOS	
■	Eletroduto Roscável
🟨	Eletroduto Corrugado Amarelo
🟦	Duto Azul TV,Dados e Telefone
🟧	Eletroduto Corrugado Reforçado Laranja

LEGENDA DE ELETRODUTOS

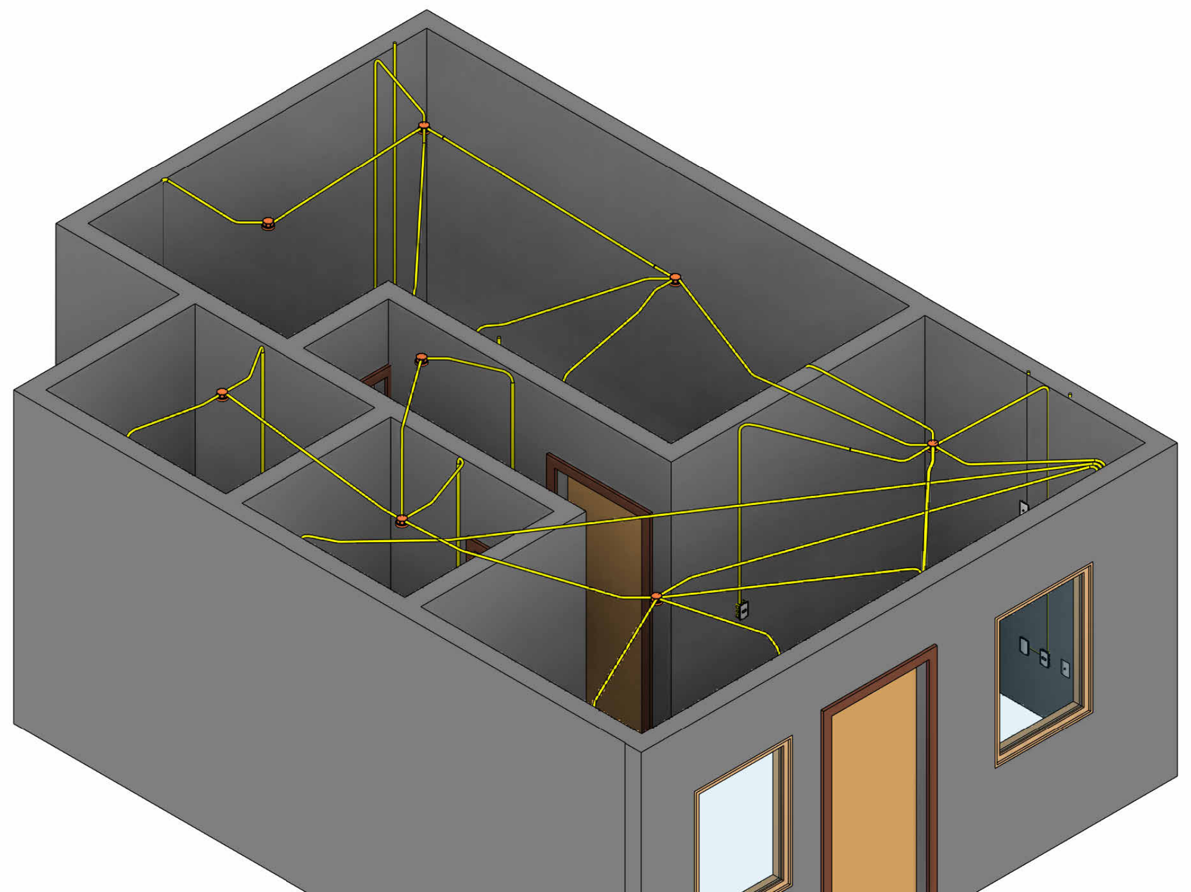

05 - PLANTA ELÉTRICA 3D

LOGOMARCA:

J.R.S

joserobson20007@gmail.com

APROVAÇÃO:

ARQUITETURA - APROVAÇÃO

Endereço:
AV. MARCONDES DE BRITO, 112
VILA MATILDE

Proprietario:
RESIDENCIAL
MATILDE VILLE

Arter do Projeto:
Jose Robson da Silva

Resp: Técnico:
Jose Robson da Silva

Descriminação Pavimentos:
SUPERIOR

Area do Terreno: 000m²

Área do Construída: 34m²

Área do Permeável: m²

FOLHA:
1 / 1

Número do TRT:CFT09600253404

Data 30 de Outubro de 2024

Escala