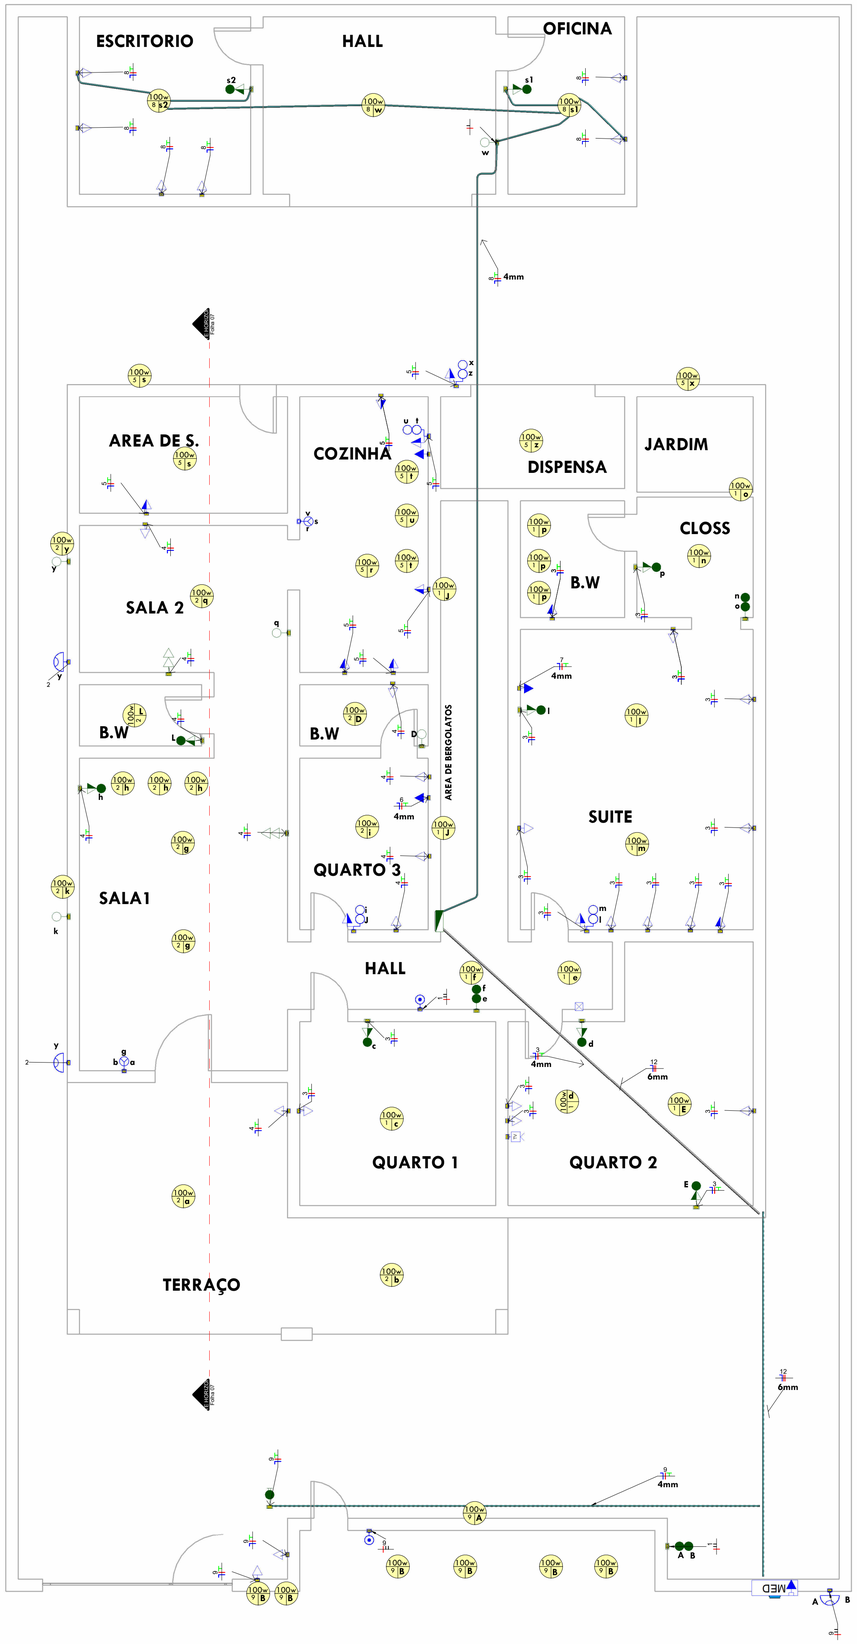


RESIDENCIAL
MATILDE VILLE – Casa 130m²

Ramal de Entrada


Concessionária: COSERN/220V

Nível de Tensão: 220V

Fases	C. fase (mm²)	C. neutro (mm²)	D. do medidor (A)	C. terra (mm²)	Disjuntor Geral (A	P.Instalada (kW)	P. Demandada (kW)
2	6	6	32	6	55	---	----

Quadro de Cargas #2

Circuito	Seção (mm²)	Disjuntor In(A)	Tensão (V)	Potência (VA)	Corrente (A)	Agrupamento	C. de Condução (A	Descrição
1	2,5	16	220	1400	6,4	3	6,4	Iluminação
2	2,5	16	220	1300	5,9	3	5,9	Iluminação
3		16	220	2300	10,5	3	10,5	Tomadas TUGs
4	2,5	16	220	2400	10,9	3	10,9	TomadaTUGs
5	2,5	16	220	3600	16,4	3	16,4	Ilumin/TUGs
6	2,5	20	220	3500	15,9	3	15,9	Ar Condicionado 1
7	4	16	220	3500	15,9	3	15,9	Ar Condicionado 2
8	4	16	220	2100	9,5	3	9,5	Escritorio/Oficina
9	4	16	220	2100	9,5	3	9,5	Motor

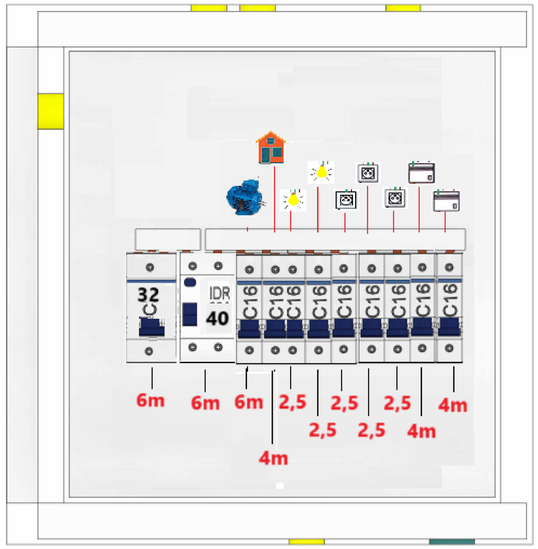

#1 VISTA 3D QDC

SIMBOLOGIA ELÉTRICA	
	Tomada Baixa 2P+T, 10A, a 0,30 m do piso, embutido em caixa 4x2
	Tomada Média 2P+T, 10A, a 1,10 m do piso, embutido em caixa 4x2
	Tomada Alta 2P+T, 10A, a 2,10 cm do piso, embutido em caixa 4x2
	Tomada Baixa 2P+T, 20A, a 0,30 m do piso, embutido em caixa 4x2
	Tomada Média 2P+T, 20A, a 1,10 m do piso , embutido em caixa 4x2
	Tomada Alta 2P+T, 20A, a 2,10 m do piso , embutido em caixa 4x2
	Tomada de Piso 2P+T, 10A
	Tomada de Teto 2P+T, 20A
	Módulo de tomada USB
	Ponto de Força com placa saída de fio, a 220cm do piso acabado
	Ponto de Força com placa saída de fio, a "x" cm do piso acabado
	Interruptor simples de uma seção, embutido em caixa 4x2
	Interruptor paralelo, embutido em caixa 4x2
	Interruptor intermediário, embutido em caixa 4x2
	Pulsador
	Ponto para campainha
	Dimer (Variador de Luminosidade)
	Sensor de presença, embutido em caixa 4x2
	Ponto de luz embutido no teto
	Ponto de luz na parede para arandela
	Ponto de luz na parede para fita LED
	Eletroduto embutido no teto ou na parede
	Eletroduto embutido no piso
	Quadro geral de luz e força embutido a 1,50 do piso acabado
MED	Caixa para medidor
	Caixa de passagem no piso
CPT	Caixa de passagem de passagem CPT de embutir na parede
	Caixa de passagem de passagem 4X2" ou 4x4" de embutir na parede
	Eletroduto que sobe
	Eletroduto que desce
	Eletroduto que passa descendo
	Eletroduto que passa subindo
	Condutores Neutro, Fase, Terra e Retorno, respectivamente
A	Simbologia de elevação

Observações:

SIMBOLOGIA ELÉTRICA

LEGENDA ELETRODUTOS
Eletroduto Roscável
Eletroduto Corrugado Amarelo
Duto Azul TV,Dados e Telefone
Eletroduto Corrugado Reforçado Laranja
Eletroduto PEAD
Cabo Bipolar
Cabo Tripolar
Eletroduto Roscável embutido no piso
Eletroduto Corrugado Amarelo embutido no piso
Duto Azul TV, Dados e Telefone embutido no piso
Eletroduto Corrugado Reforçado Laranja embutido no piso
Eletroduto PEAD embutido no piso
Cabo Bipolar embutido no piso
Cabo Tripolar embutido no piso

LEGENDA DE ELETRODUTOS



CORTE HORIZONTAL

LOGOMARCA:

J.R.S

joserobson20007@gmail.com

APROVAÇÃO:

ELETRÍCA - APROVAÇÃO

Endereço:
AV. MARCONDES DE BRITO, 112
VILA MATILDE

Proprietario:
LAECIO

Arter do Projeto:
Jose Robson da Silva

Resp: Técnico:
Jose Robson da Silva

Descriminação Pavimentos:
Térreo,

Area do Terreno: 000m²

Area do Construida: 130m²

Área do Permeável: m²

FOLHA:
1 / 1

Número do :CFT: 09600253404

Data 05 de JULHO de 2025

Escala